



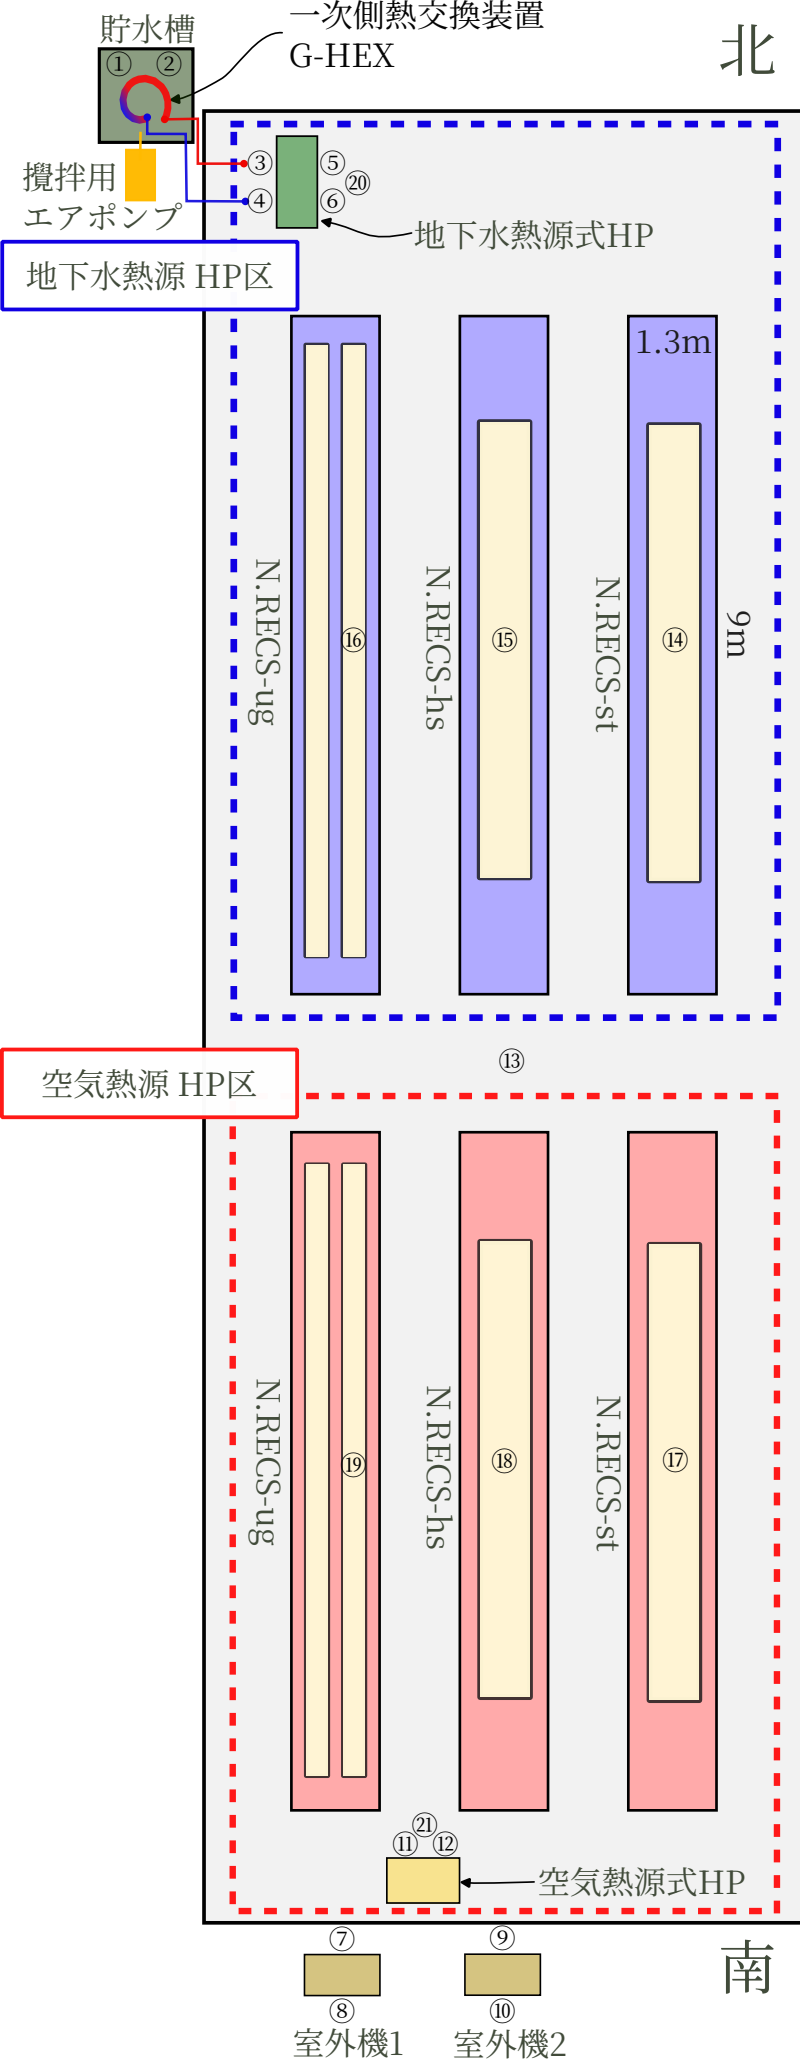

- N.RECS-st : 標準型N.RECS
栽培槽のサイズ : $0.9 \times 6\text{m}$
実効栽培面積 : 4.5 m^2
- N.RECS-hs : 蓄熱型N.RECS
栽培槽のサイズ : $0.9 \times 6\text{m}$
実効栽培面積 : 4.5 m^2
- N.RECS-ug : U字溝型N.RECS
栽培槽のサイズ : $0.2 \times 8\text{m} \times 2\text{本}$
実効栽培面積 : 3.2 m^2

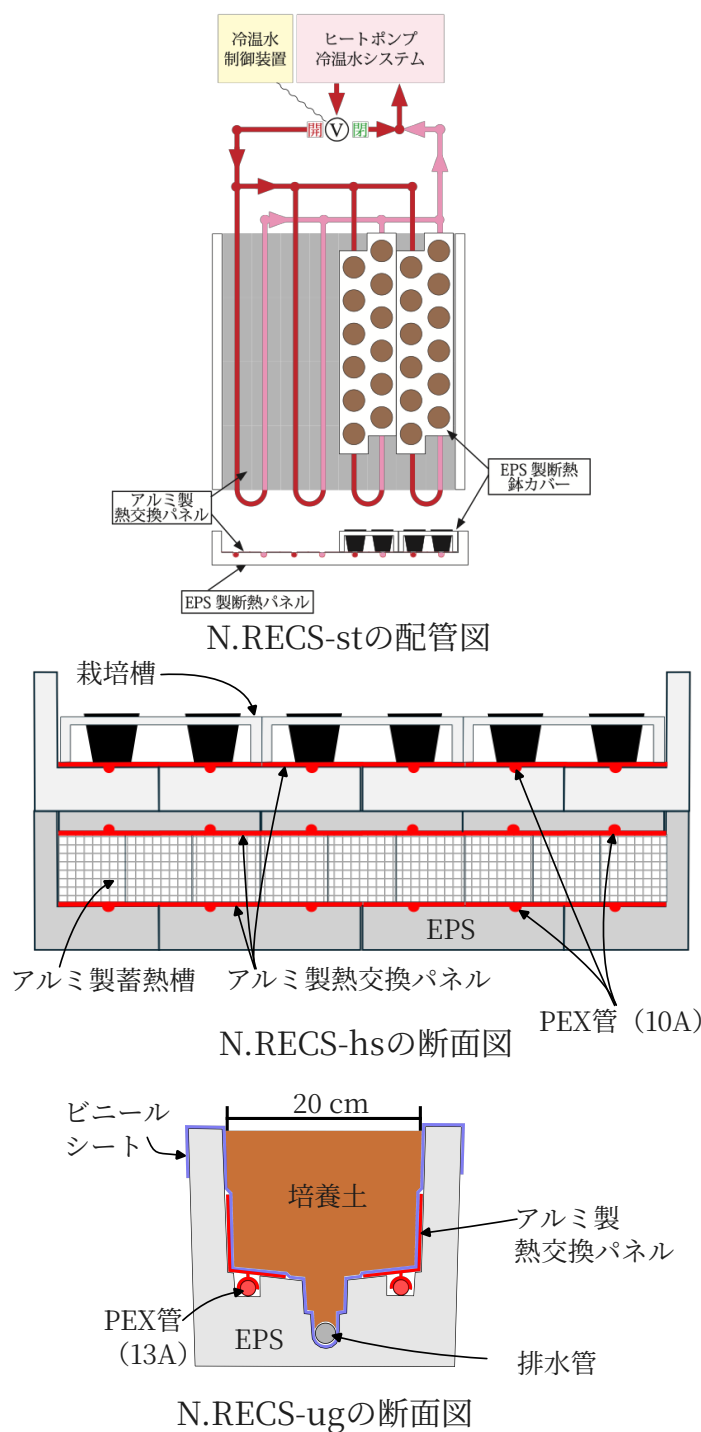

図中の①～⑳はセンサーの設置位置を示す。