


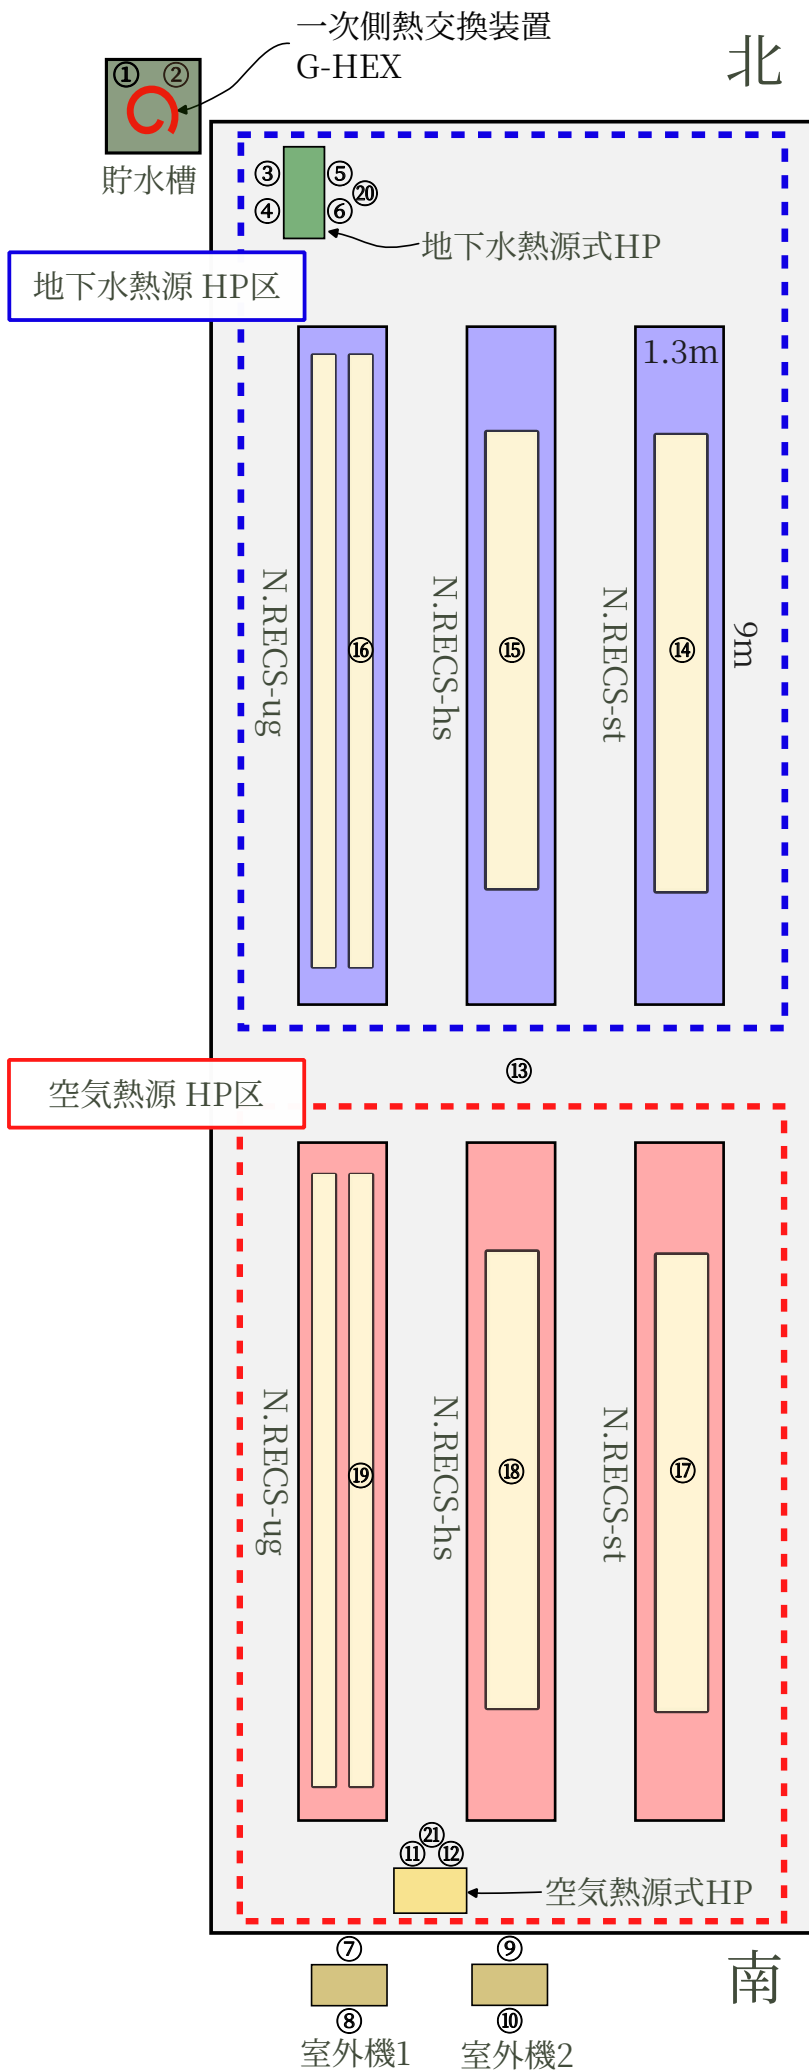

N.RECS-st : 標準型N.RECS

栽培槽のサイズ: $0.9 \times 6\text{m}$

実効栽培面積: 4.5m^2

N.RECS-hs : 蓄熱型N.RECS


栽培槽のサイズ: $0.9 \times 6\text{m}$

実効栽培面積: 4.5m^2

N.RECS-ug : U字溝型N.RECS

栽培槽のサイズ: $0.2 \times 8\text{m} \times 2\text{本}$

実効栽培面積: 3.2m^2

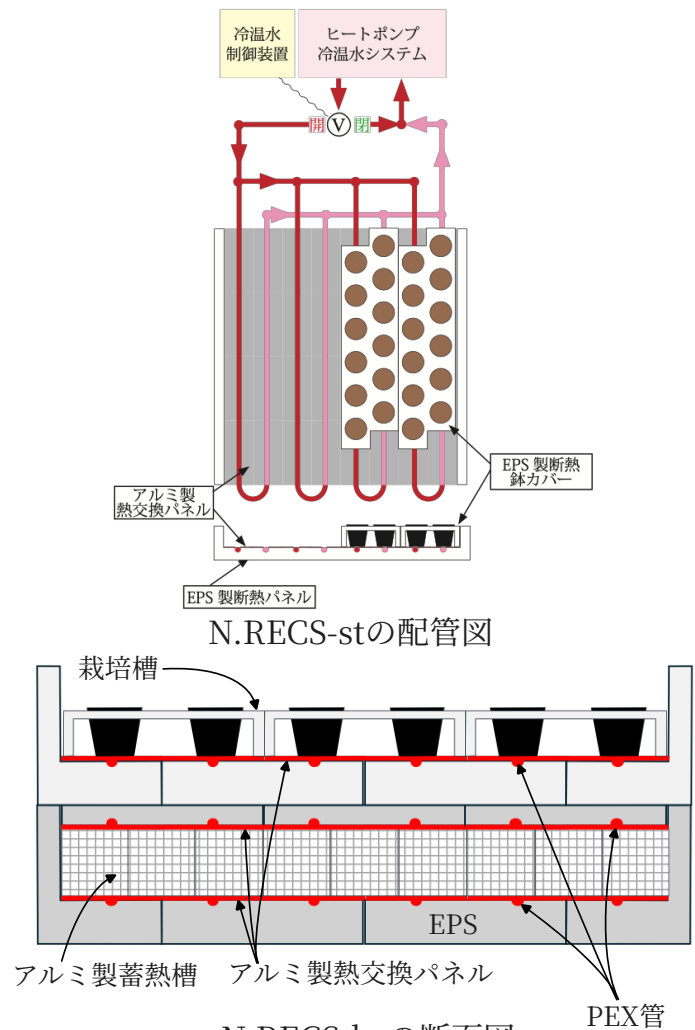

図中の①～㉑はセンサを設置位置を示す。